


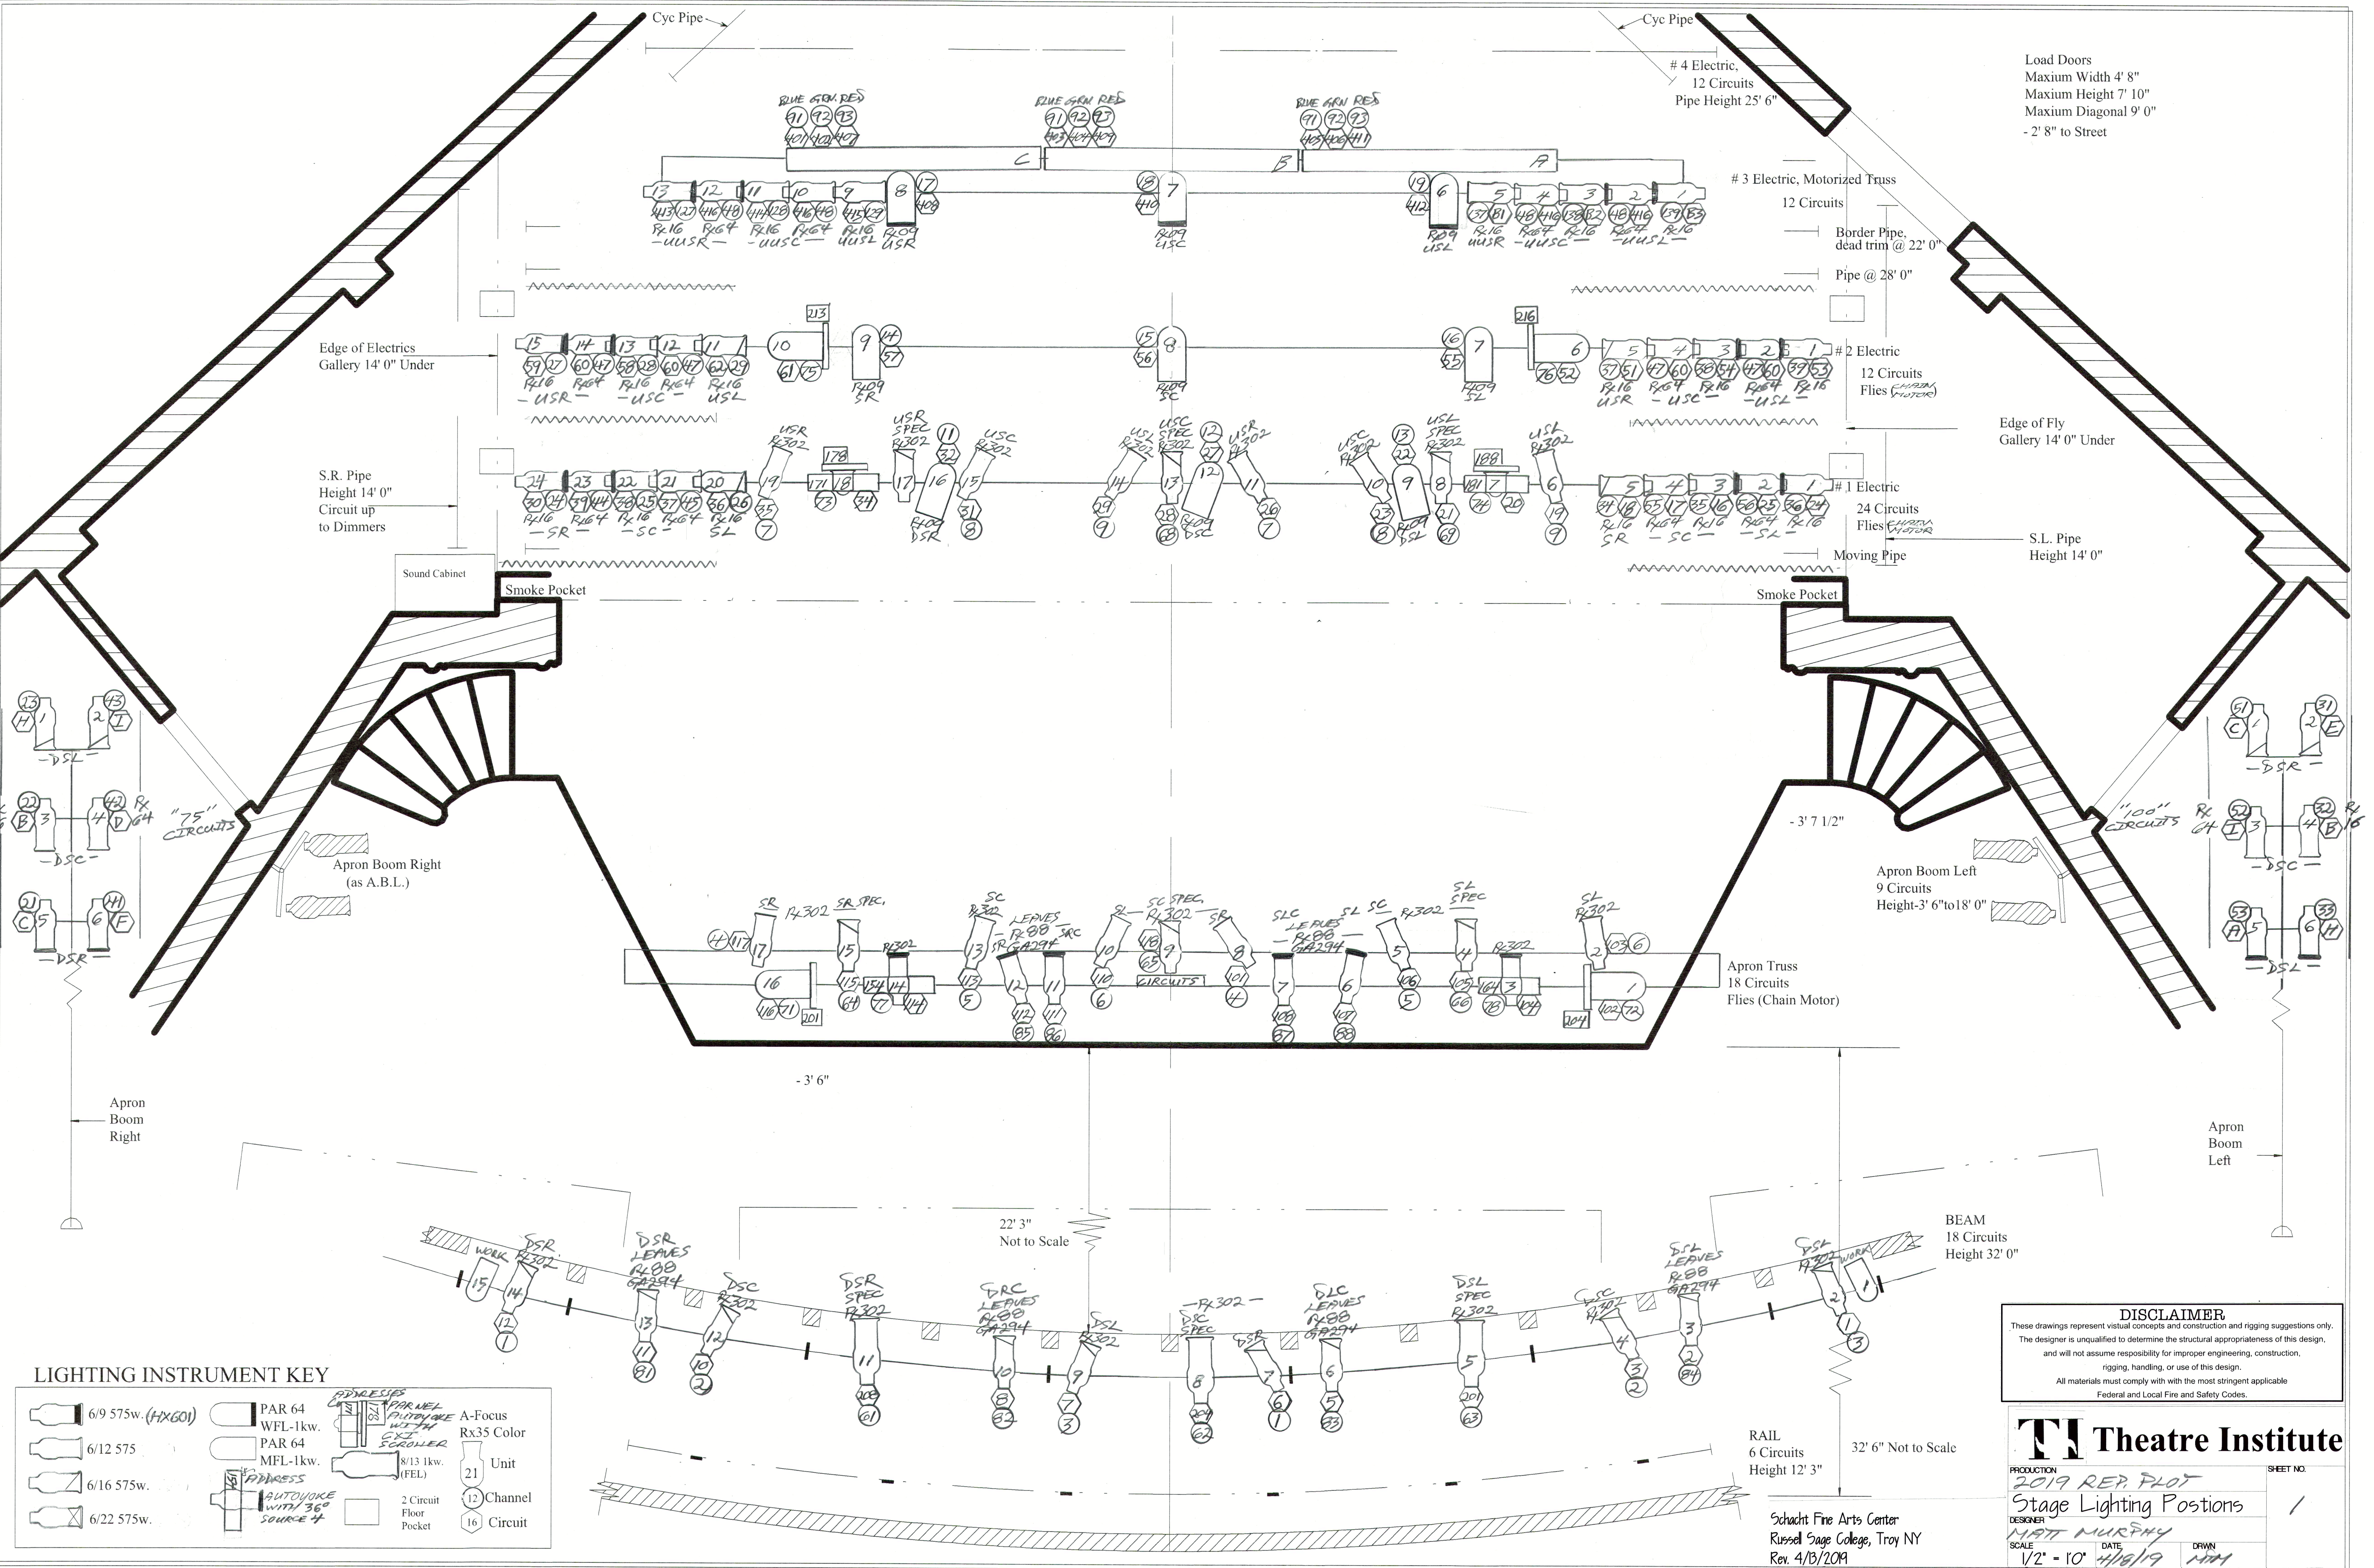

Load Doors
Maxium Width 4' 8"
Maxium Height 7' 10"
Maxium Diagonal 9' 0"
- 2' 8" to Street

DISCLAIMER
These drawings represent visual concepts and construction and rigging suggestions only.
The designer is unqualified to determine the structural appropriateness of this design,
and will not assume responsibility for improper engineering, construction,
rigging, handling, or use of this design.
All materials must comply with the most stringent applicable
Federal and Local Fire and Safety Codes.

T Theatre Institute
PRODUCTION
2019 REP. FLOT
Stage Lighting Positions
DESIGNER
NAT MURPHY
SCALE
1/2" = 10'
DATE
4/18/19
DRAWN
NAT

SHEET NO.
1

LIGHTING INSTRUMENT KEY

6/9 575w. (HX601)
 6/12 575
 6/16 575w.
 6/22 575w.

PAR 64 WFL-1kw.
 PAR 64 MFL-1kw.
 ADDRESS AUTO/JOKE WITH 360 SOURCE #
 2 Circuit Floor Pocket

A-Focus Rx35 Color
 Unit 21
 12 Channel
 16 Circuit

Schacht Fine Arts Center
Russell Sage College, Troy NY
Rev. 4/13/2019